


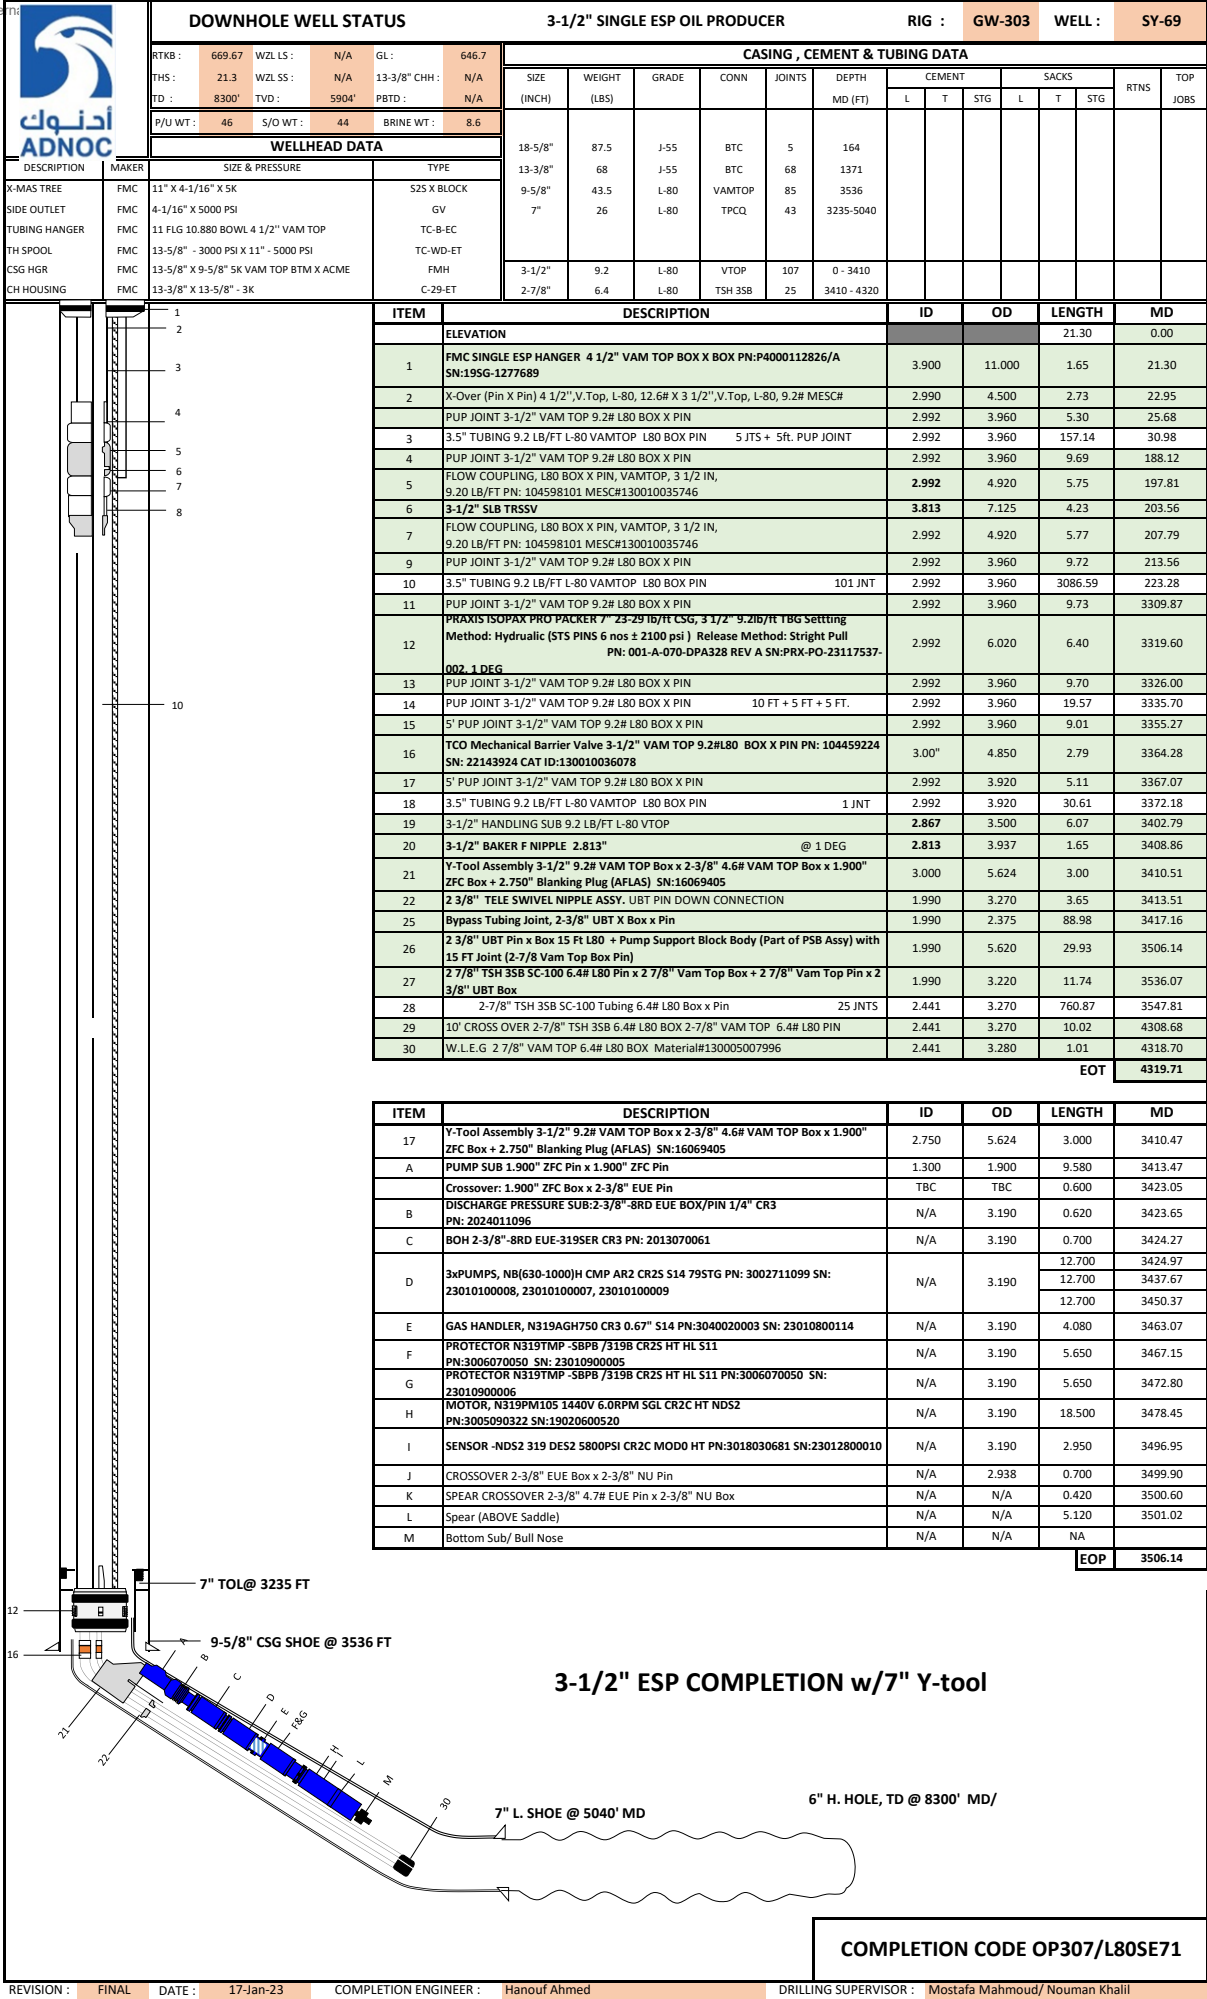

7" TOL @ 3235 FT

9-5/8" CSG SHOE @ 3536 FT

7" L. SHOE @ 5040' MD

6" H. HOLE, TD @ 8300' MD/

3-1/2" ESP COMPLETION w/7" Y-tool

COMPLETION CODE OP307/L80SE71

REVISION : FINAL

DATE : 17-Jan-23

COMPLETION ENGINEER : Hanouf Ahmed

DRILLING SUPERVISOR : Mostafa Mahmoud/ Nouman Khalil